



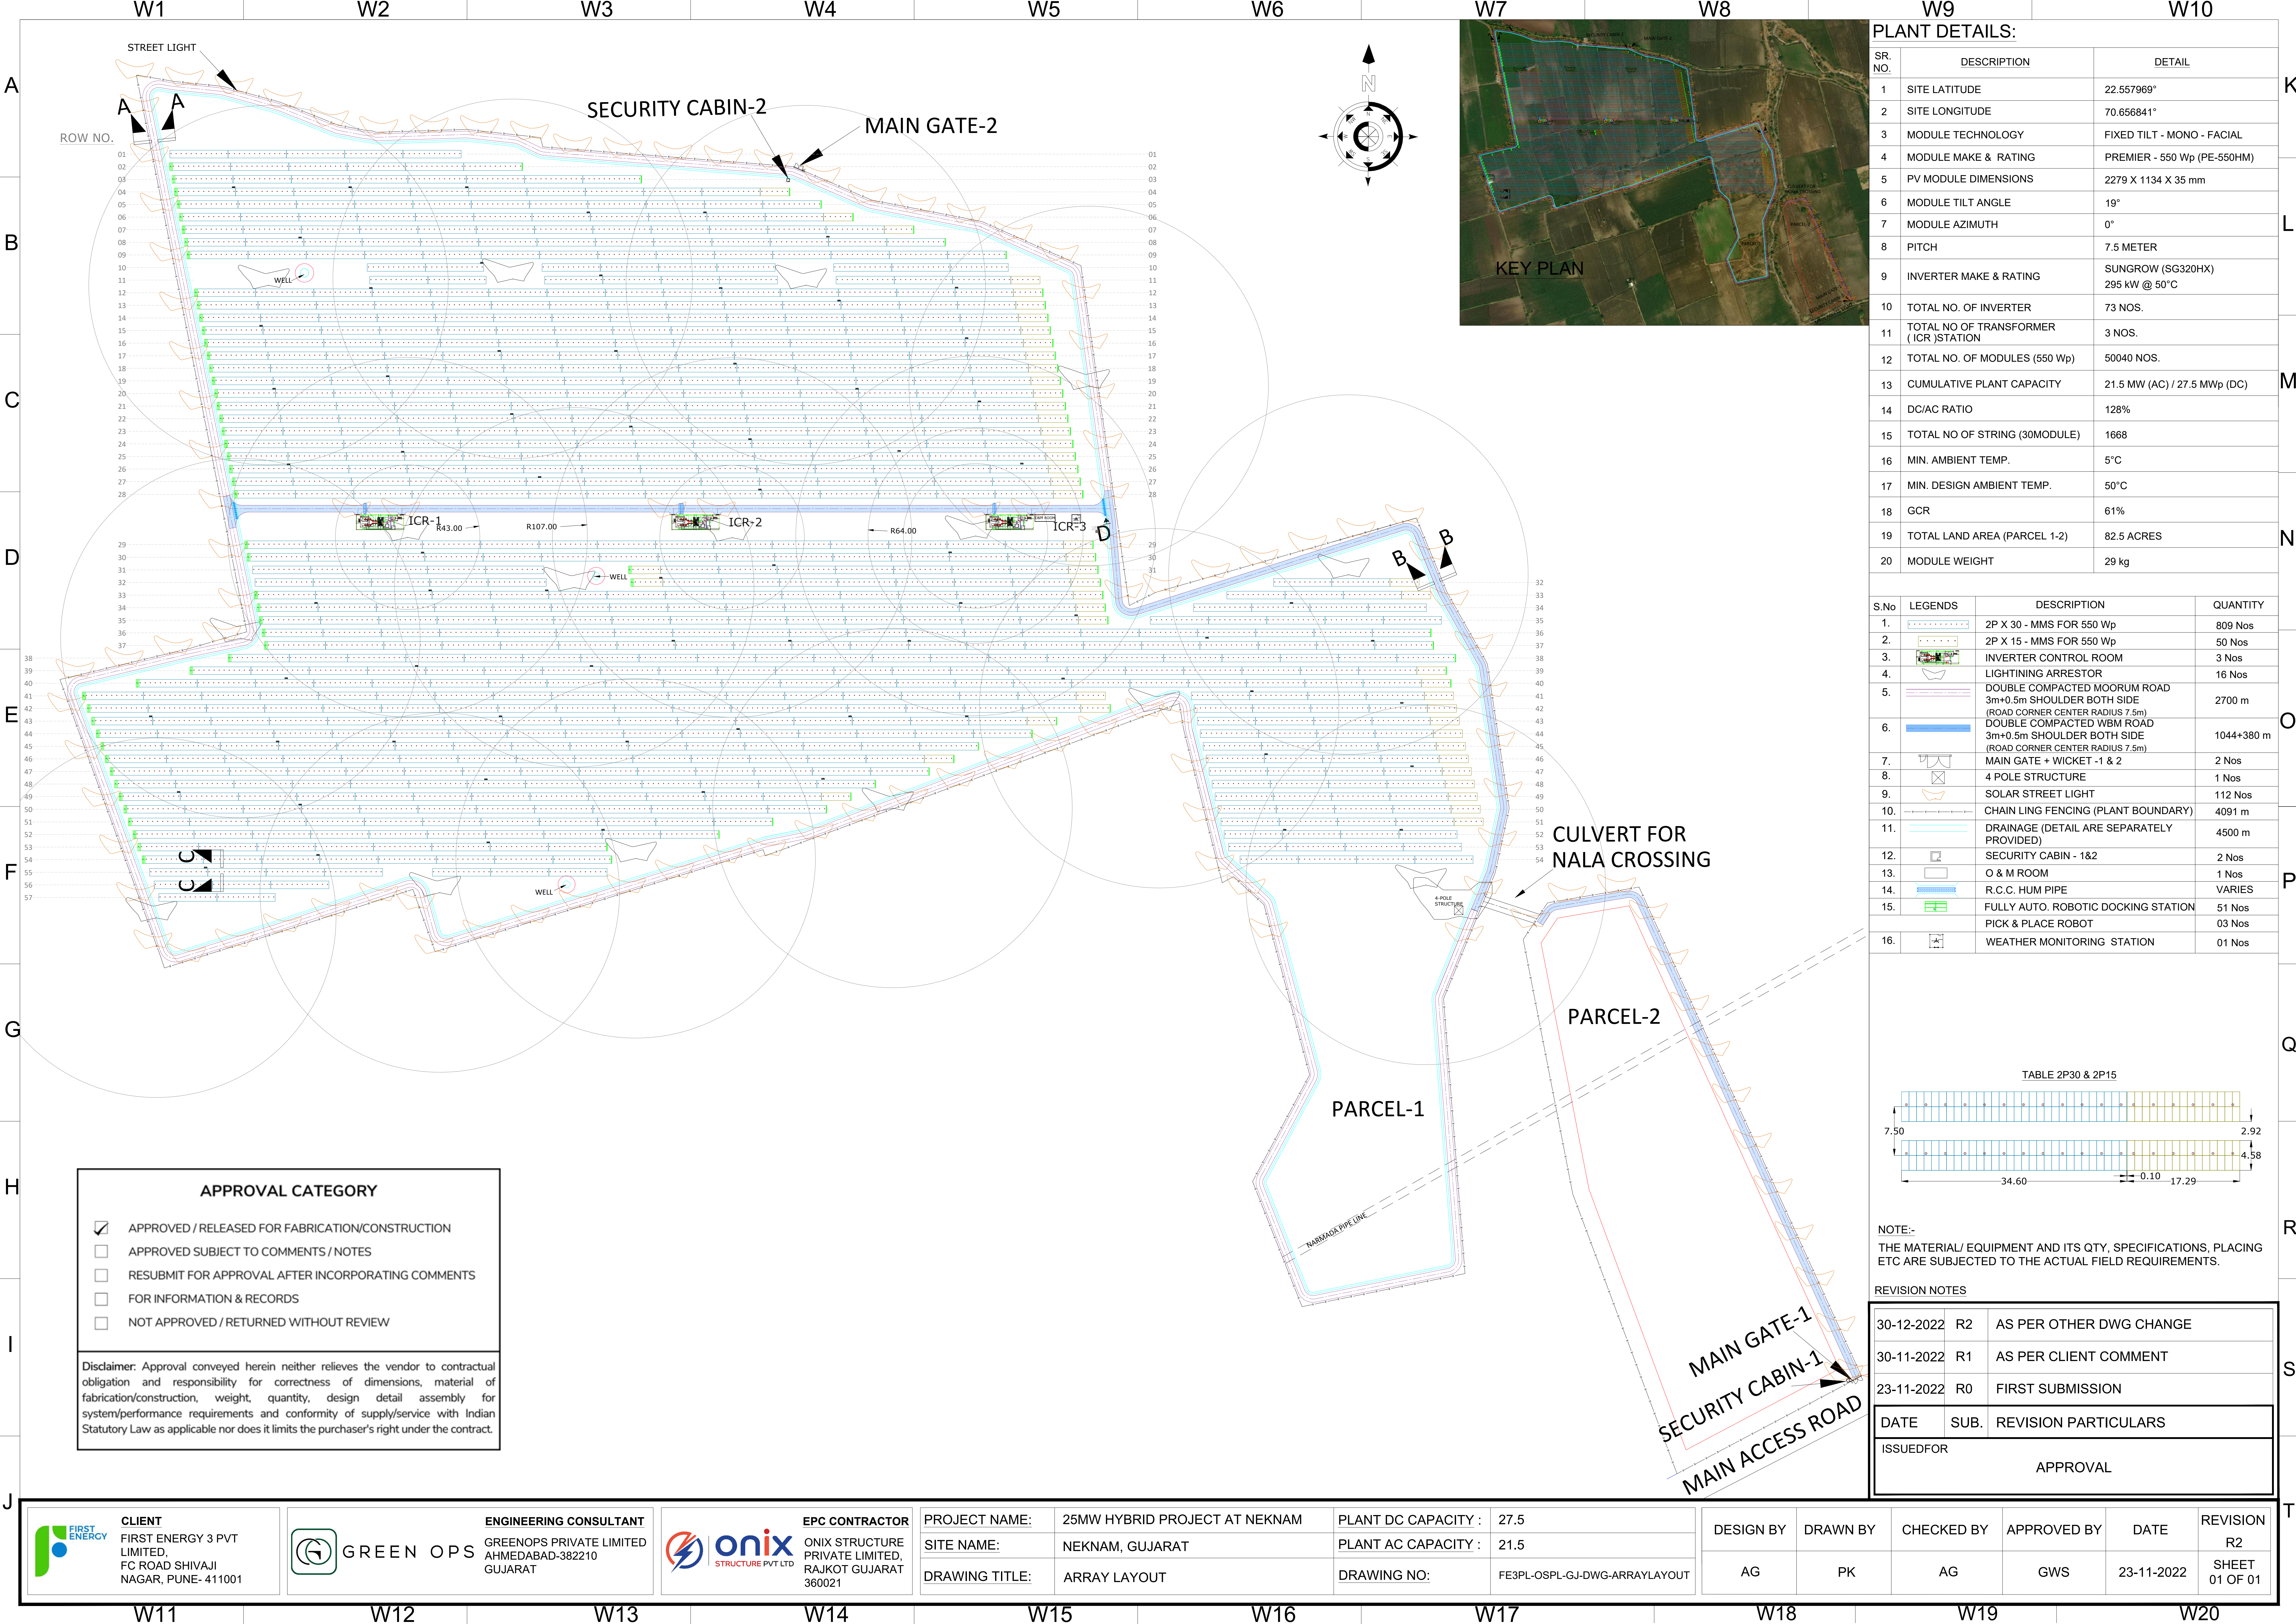

PLANT DETAILS:		
Sr. No.	DESCRIPTION	DETAIL
1	SITE LATITUDE	22.557969°
2	SITE LONGITUDE	70.656841°
3	MODULE TECHNOLOGY	FIXED TILT - MONO - FACIAL
4	MODULE MAKE & RATING	PREMIER - 550 Wp (PE-550HM)
5	PV MODULE DIMENSIONS	2279 X 1134 X 35 mm
6	MODULE TILT ANGLE	19°
7	MODULE AZIMUTH	0°
8	PITCH	7.5 METER
9	INVERTER MAKE & RATING	SUNGROW (SG320HX) 295 kW @ 50°C
10	TOTAL NO. OF INVERTER	73 NOS.
11	TOTAL NO OF TRANSFORMER (ICR) STATION	3 NOS.
12	TOTAL NO. OF MODULES (550 Wp)	50040 NOS.
13	CUMULATIVE PLANT CAPACITY	21.5 MW (AC) / 27.5 MWp (DC)
14	DC/AC RATIO	128%
15	TOTAL NO OF STRING (30MODULE)	1668
16	MIN. AMBIENT TEMP.	5°C
17	MIN. DESIGN AMBIENT TEMP.	50°C
18	GCR	61%
19	TOTAL LAND AREA (PARCEL 1-2)	82.5 ACRES
20	MODULE WEIGHT	29 kg

S.No	LEGENDS	DESCRIPTION	QUANTITY
1.		2P X 30 - MMS FOR 550 Wp	809 Nos
2.		2P X 15 - MMS FOR 550 Wp	50 Nos
3.		INVERTER CONTROL ROOM	3 Nos
4.		LIGHTNING ARRESTOR	16 Nos
5.		DOUBLE COMPACTED MOORUM ROAD 3m+0.5m SHOULDER BOTH SIDE (ROAD CORNER CENTER RADIUS 7.5m)	2700 m
6.		DOUBLE COMPACTED WBM ROAD 3m+0.5m SHOULDER BOTH SIDE (ROAD CORNER CENTER RADIUS 7.5m)	1044+380 m
7.		MAIN GATE + WICKET - 1 & 2	2 Nos
8.		4 POLE STRUCTURE	1 Nos
9.		SOLAR STREET LIGHT	112 Nos
10.		CHAIN LINK FENCING (PLANT BOUNDARY)	4091 m
11.		DRAINAGE (DETAIL ARE SEPARATELY PROVIDED)	4500 m
12.		SECURITY CABIN - 1&2	2 Nos
13.		O & M ROOM	1 Nos
14.		R.C.C. HUM PIPE	VARIES
15.		FULLY AUTO. ROBOTIC DOCKING STATION	51 Nos
		PICK & PLACE ROBOT	03 Nos
16.		WEATHER MONITORING STATION	01 Nos

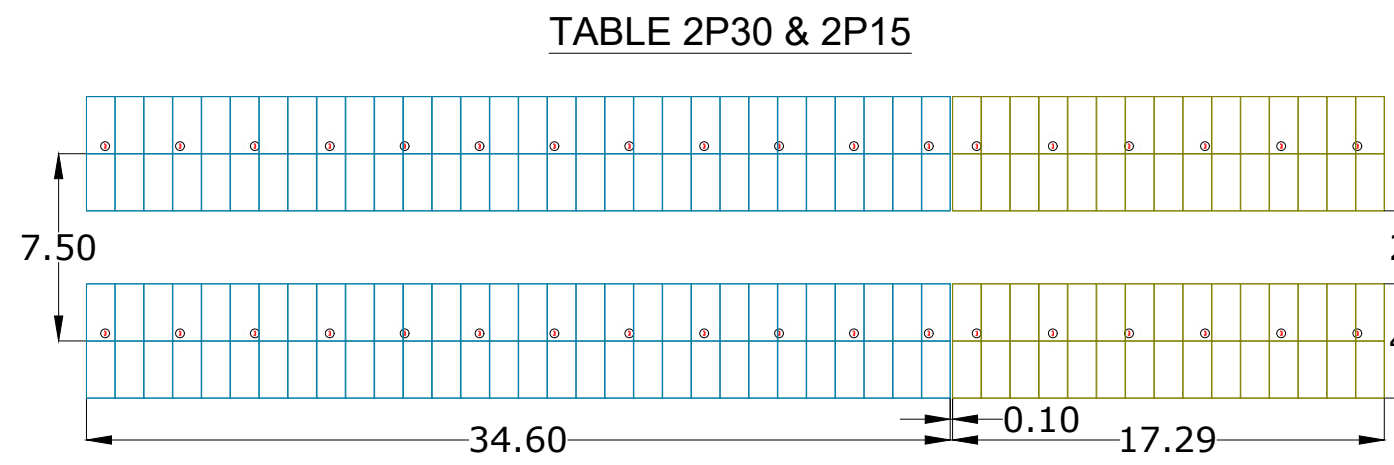

NOTE:-
THE MATERIAL/ EQUIPMENT AND ITS QTY, SPECIFICATIONS, PLACING ETC ARE SUBJECTED TO THE ACTUAL FIELD REQUIREMENTS.

REVISION NOTES			
30-12-2022	R2	AS PER OTHER DWG CHANGE	
30-11-2022	R1	AS PER CLIENT COMMENT	
23-11-2022	R0	FIRST SUBMISSION	
DATE	SUB.	REVISION PARTICULARS	
ISSUED FOR		APPROVAL	

APPROVAL CATEGORY

☒

APPROVED / RELEASED FOR FABRICATION/CONSTRUCTION

☐ APPROVED SUBJECT TO COMMENTS / NOTES

☐ RESUBMIT FOR APPROVAL AFTER INCORPORATING COMMENTS

☐ FOR INFORMATION & RECORDS

☐ NOT APPROVED / RETURNED WITHOUT REVIEW

Disclaimer: Approval conveyed herein neither relieves the vendor to contractual obligation and responsibility for correctness of dimensions, material of fabrication/construction, weight, quantity, design detail assembly for system/performance requirements and conformity of supply/service with Indian Statutory Law as applicable nor does it limits the purchaser's right under the contract.

CLIENT
FIRST ENERGY 3 PVT
LIMITED
FC ROAD SHIVAJI
NAGAR, PUNE- 411001

ENGINEERING CONSULTANT
GREENOPS PRIVATE LIMITED
AHMEDABAD-382210
GUJARAT

EPC CONTRACTOR
ONIX STRUCTURE
PRIVATE LIMITED,
RAJKOT GUJARAT
360021

PROJECT NAME:	25MW HYBRID PROJECT AT NEKNAM
SITE NAME:	NEKNAM, GUJARAT
DRAWING TITLE:	ARRAY LAYOUT

PLANT DC CAPACITY :	27.5
PLANT AC CAPACITY :	21.5
DRAWING NO:	FE3PL-OSPL-GJ-DWG-ARRAYLAYOUT

DESIGN BY	DRAWN BY	CHECKED BY	APPROVED BY	DATE	REVISION
AG	PK	AG	GWS	23-11-2022	R2
					SHEET 01 OF 01

